


Room	Manifold		Balance	Flow Rate	Circuit Length	Pipe Spacing	Heating Area	Floor Temp	Mean Water Temp	Output Per Area	Room Area	Room Design Temp	Room Heatloss	Room Design Output
Kitchen	Manifold G-1	1	10.0kPa (Index)	1.18L/min	68.5m	200mm	23.9m²	27.8°C	45.0°C	64.6W/m²	27.1m²	21.0°C	1545.8W	1545.8W
Kitchen	Manifold G-1	2	11.1kPa	1.06L/min	61.3m	200mm	20.0m²	27.8°C	45.0°C	64.6W/m²	27.1m²	21.0°C	1545.8W	1545.8W
Bath	Manifold G-1	3	13.4kPa	0.54L/min	37.0m	200mm	5.9m²	28.5°C	45.0°C	63.3W/m²	5.9m²	22.0°C	370.9W	370.9W
Bedroom	Manifold G-1	4	12.7kPa	0.61L/min	61.6m	200mm	10.9m²	25.6°C	45.0°C	38.5W/m²	10.9m²	18.0°C	420.6W	420.6W
Shower	Manifold G-1	5	13.7kPa	0.32L/min	32.3m	200mm	3.3m²	28.5°C	45.0°C	66.6W/m²	4.2m²	22.0°C	220.2W	220.2W
Bedroom	Manifold G-1	6	10.8kPa	0.91L/min	81.6m	200mm	14.8m²	25.6°C	45.0°C	42.5W/m²	16.1m²	18.0°C	630.6W	630.6W
Hall	Manifold G-1	7	13.6kPa	0.46L/min	28.4m	200mm	8.6m²	25.6°C	45.0°C	36.5W/m²	8.6m²	18.0°C	315.5W	315.5W

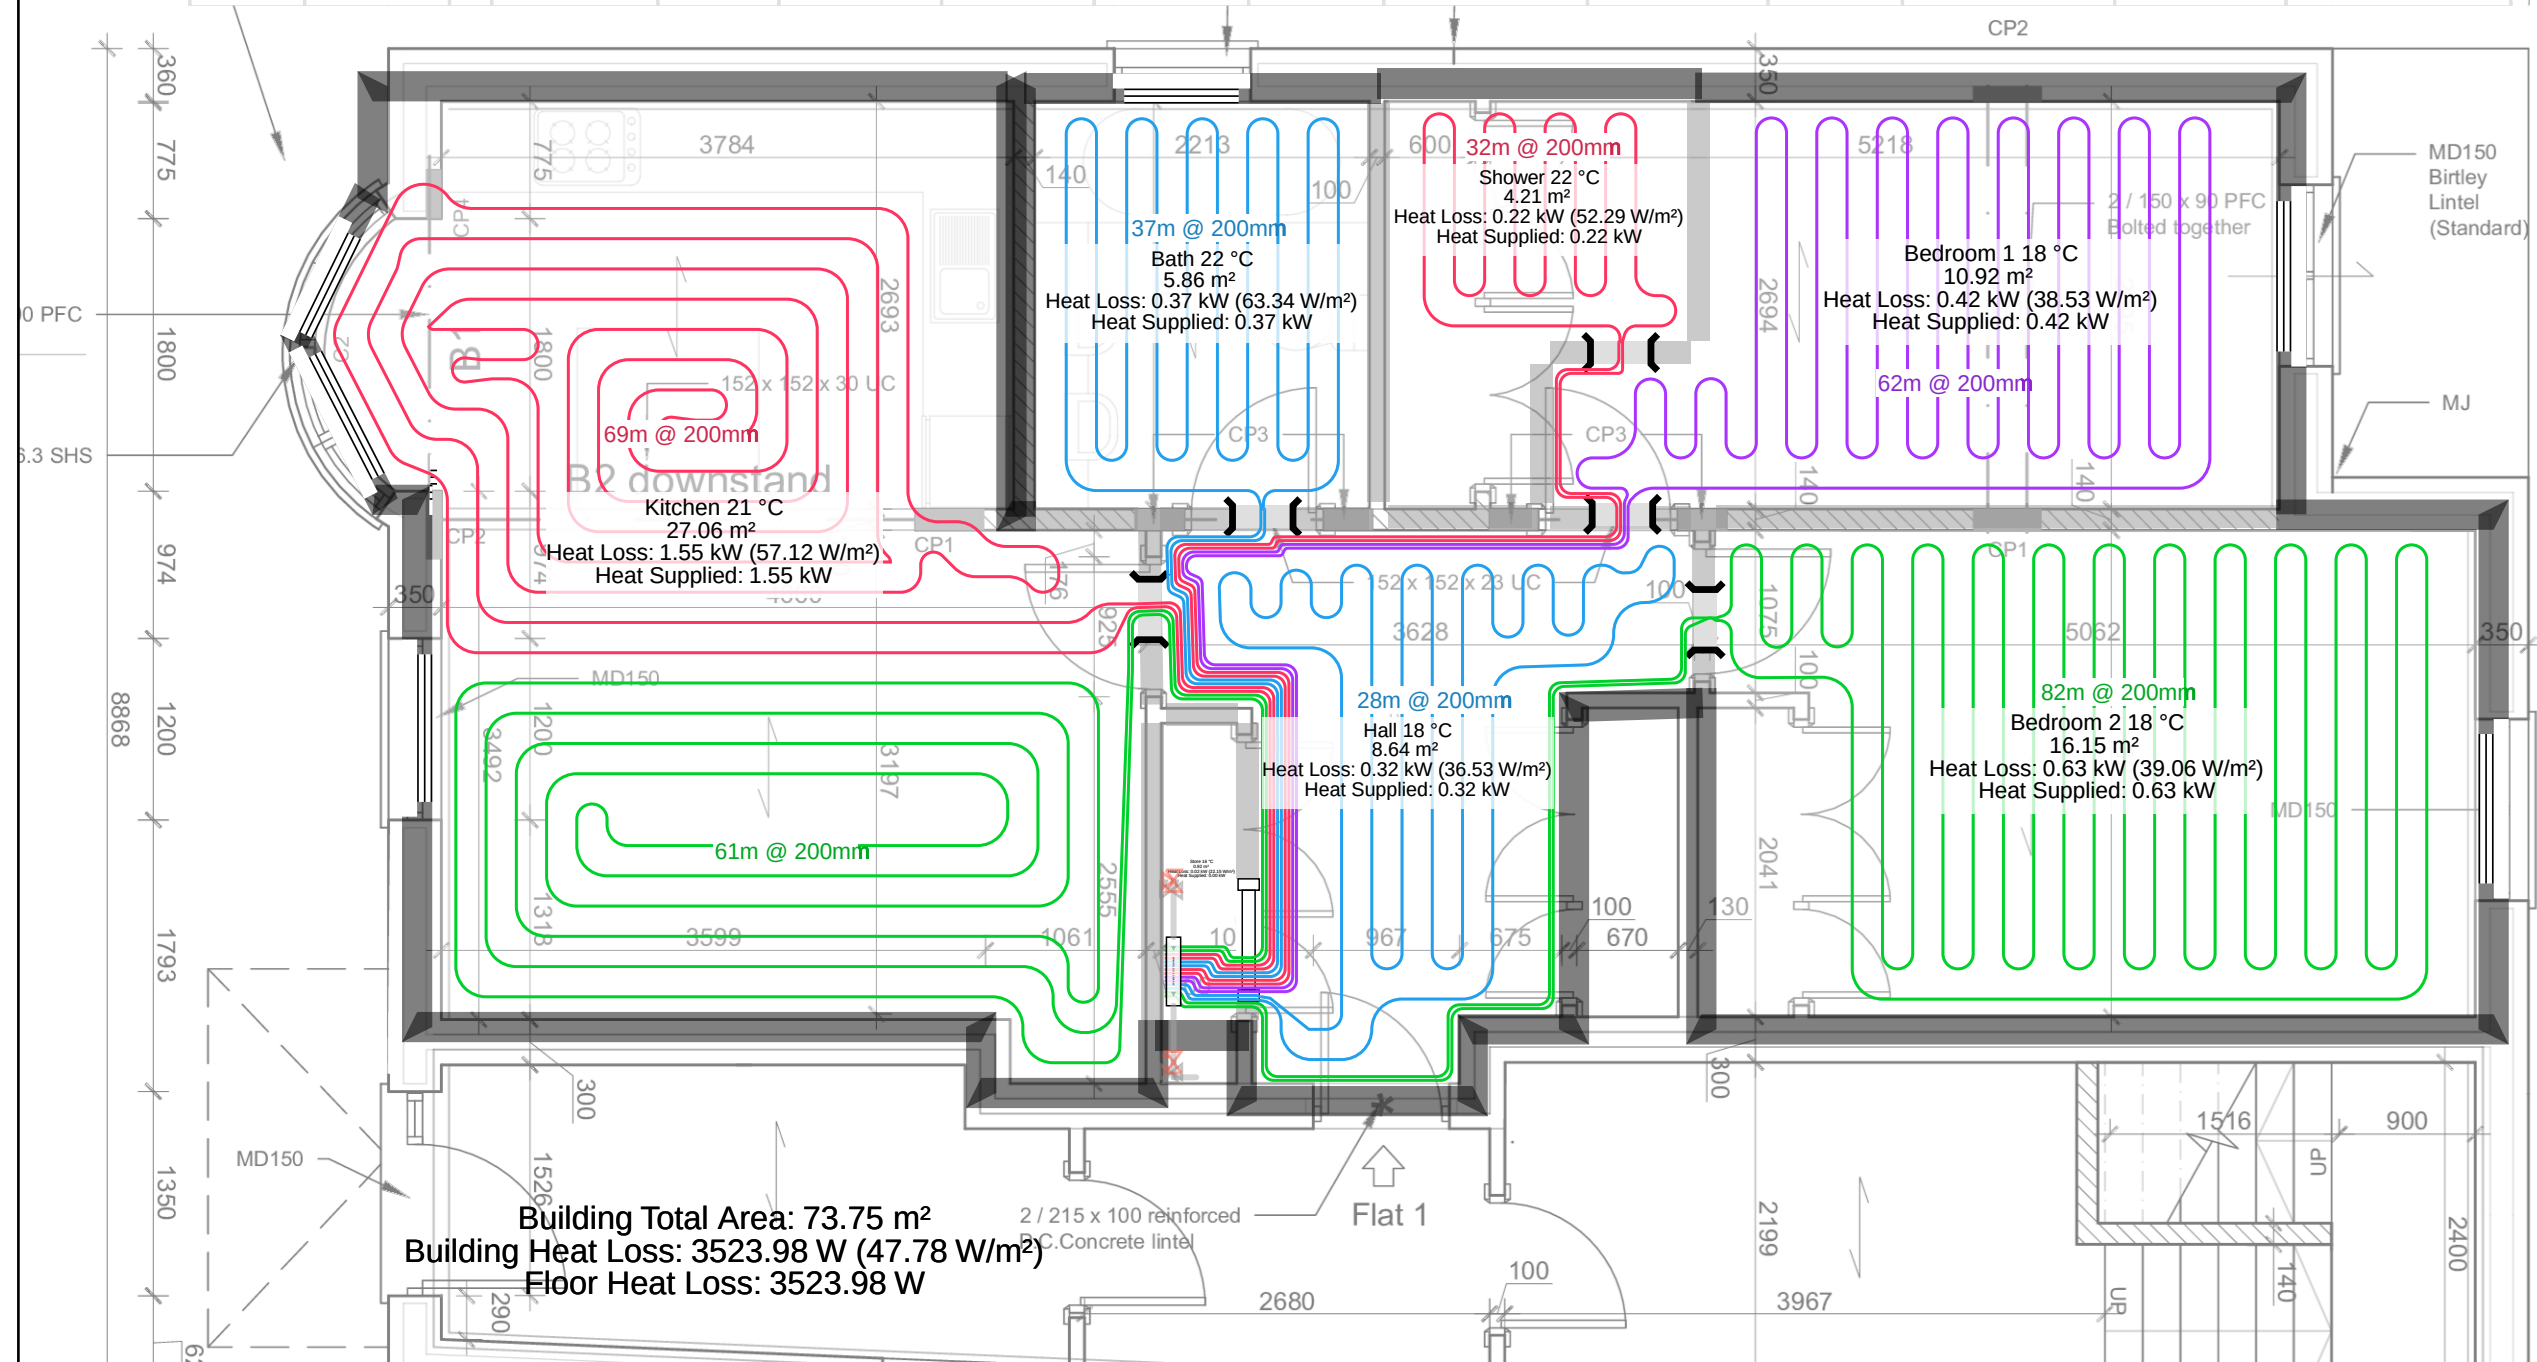

Revision:	Description:	Date:
1		26 Jun

YOUR LOGO
HERE

CLIENT:

PROJECT:
123 UFH St

GROUND MECHANICAL SERVICES

PROJECT NO.:	5
DESIGNER:	
REVIEWER:	
APPROVER:	
SCALE:	1:50 @ A3